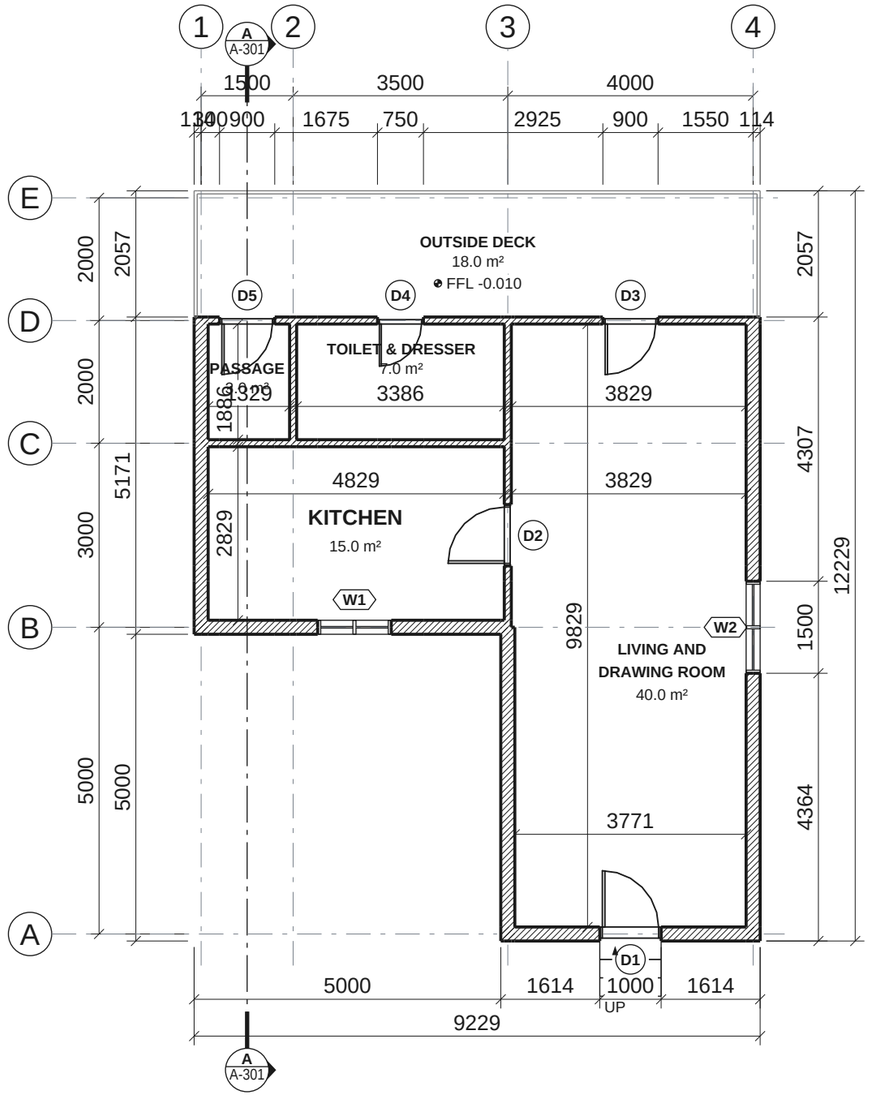

1 GROUND FLOOR PLAN

SCALE 1 : 100

DOOR & WINDOW SCHEDULE

MARK	W × H	SILL	HEAD	LOCATION
D1	1000 × 2100	—	2100	LIVING AND DRA…
D2	1000 × 2100	—	2100	KITCHEN
D3	900 × 2100	—	2100	LIVING AND DRA…
D4	750 × 2100	—	2100	TOILET & DRES…
D5	900 × 2100	—	2100	PASSAGE

MARK	W × H	SILL	HEAD	LOCATION
W1	1200 × 1300	900	2200	KITCHEN
W2	1500 × 1300	900	2200	LIVING AND DRA…

SIZES IN MM; SILL AND HEAD FROM FFL.

N

GENERAL NOTES

1. ALL DIMENSIONS ARE IN MILLIMETRES; LEVELS ARE IN METRES FROM FFL ±0.000.
2. DO NOT SCALE FROM THIS DRAWING. USE FIGURED DIMENSIONS ONLY.
3. VERIFY ALL DIMENSIONS ON SITE BEFORE WORK AND REPORT ANY DISCREPANCY TO THE ARCHITECT.
4. READ WITH ALL SHEETS OF THIS SET. DOOR AND WINDOW MARKS AS THE SCHEDULE ON A-101.
5. WALLS 230 EXTERNAL / 115 INTERNAL BRICKWORK (HATCHED); COLUMNS, BEAMS, SLABS, LINTELS AND SILLS RCC (SOLID GREY).
6. BEAMS INDICATIVE: ROOF BEAMS 230 x 600 OVERALL INCL. SLAB; PLINTH BEAM 230 x 300. TO STRUCTURAL ENGINEER'S DESIGN.

PROJECT: STUDIO APARTMENT 101					1ST
DRAWING TITLE: GROUND FLOOR PLAN			DRAWING NO.: A-101	STATUS: S2	REV: P01
DRAWN: SKETCH2MODEL	CHK'D: AUTOMATED	APPR'D: PENDING	DATE: 2026-10-18	SCALE: 1 : 100	SHEET: 1 / 4

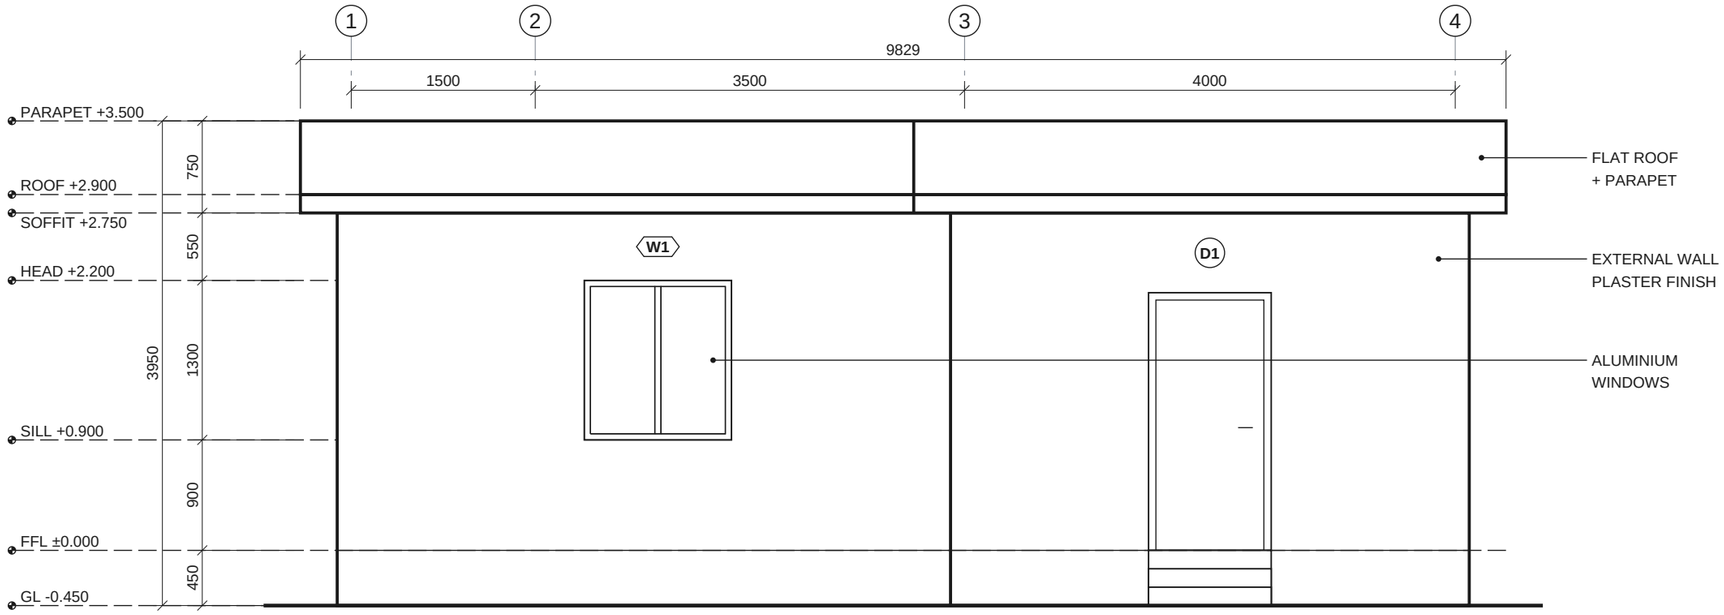

1 SOUTH ELEVATION

SCALE 1 : 50

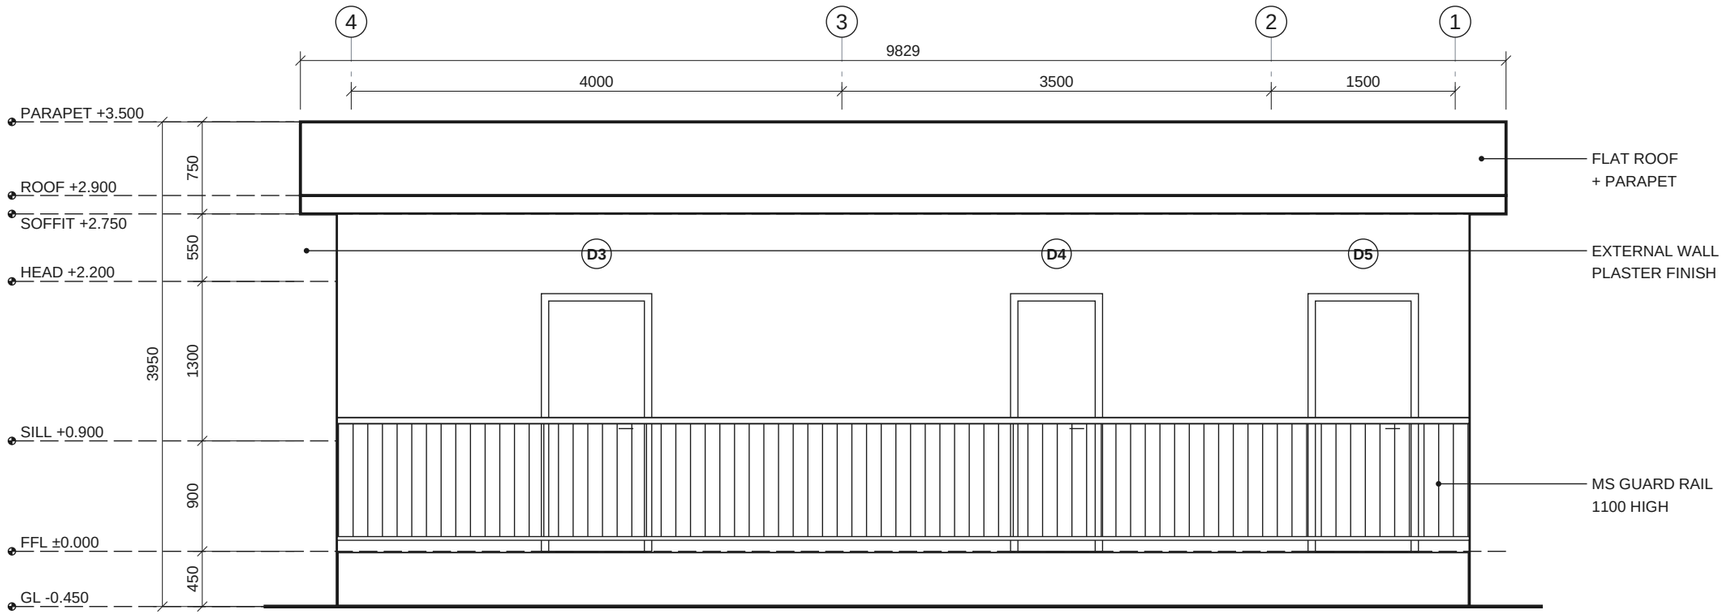

2 NORTH ELEVATION

SCALE 1 : 50

GENERAL NOTES

1. ALL DIMENSIONS ARE IN MILLIMETRES; LEVELS ARE IN METRES FROM FFL ±0.000.
2. DO NOT SCALE FROM THIS DRAWING. USE FIGURED DIMENSIONS ONLY.
3. VERIFY ALL DIMENSIONS ON SITE BEFORE WORK AND REPORT ANY DISCREPANCY TO THE ARCHITECT.
4. READ WITH ALL SHEETS OF THIS SET. DOOR AND WINDOW MARKS AS THE SCHEDULE ON A-101.
5. WALLS 230 EXTERNAL / 115 INTERNAL BRICKWORK (HATCHED); COLUMNS, BEAMS, SLABS, LINTELS AND SILLS RCC (SOLID GREY).
6. BEAMS INDICATIVE: ROOF BEAMS 230 x 600 OVERALL INCL. SLAB; PLINTH BEAM 230 x 300. TO STRUCTURAL ENGINEER'S DESIGN.

PROJECT: STUDIO APARTMENT 101					1ST
DRAWING TITLE: SOUTH AND NORTH ELEVATIONS			DRAWING NO.: A-201	STATUS: S2	REV: P01
DRAWN: SKETCH2MODEL	CHK'D: AUTOMATED	APPR'D: PENDING	DATE: 2026-10-18	SCALE: 1 : 50	SHEET: 2 / 4

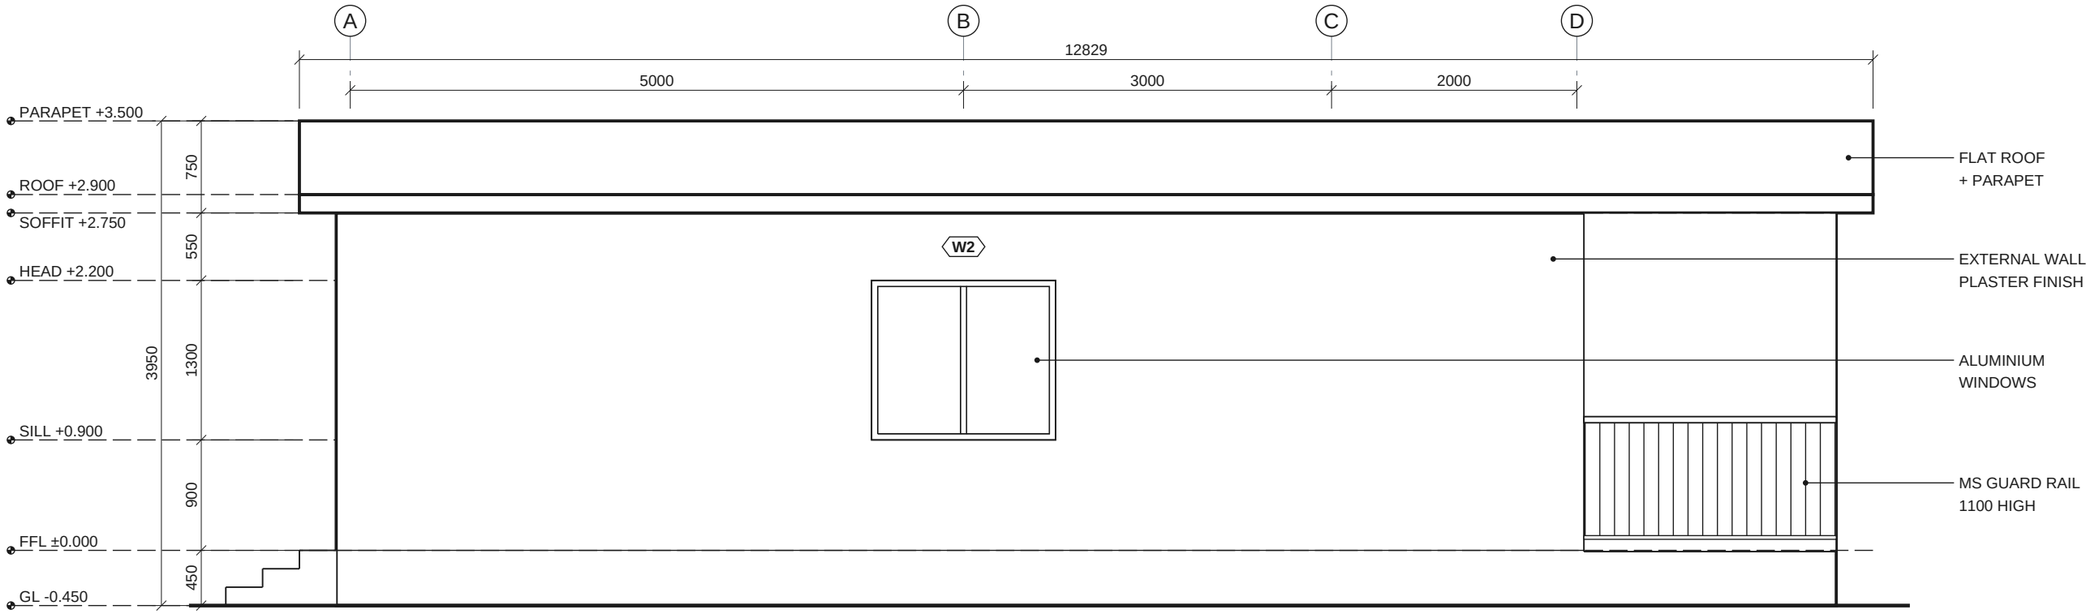

1 EAST ELEVATION

SCALE 1 : 50

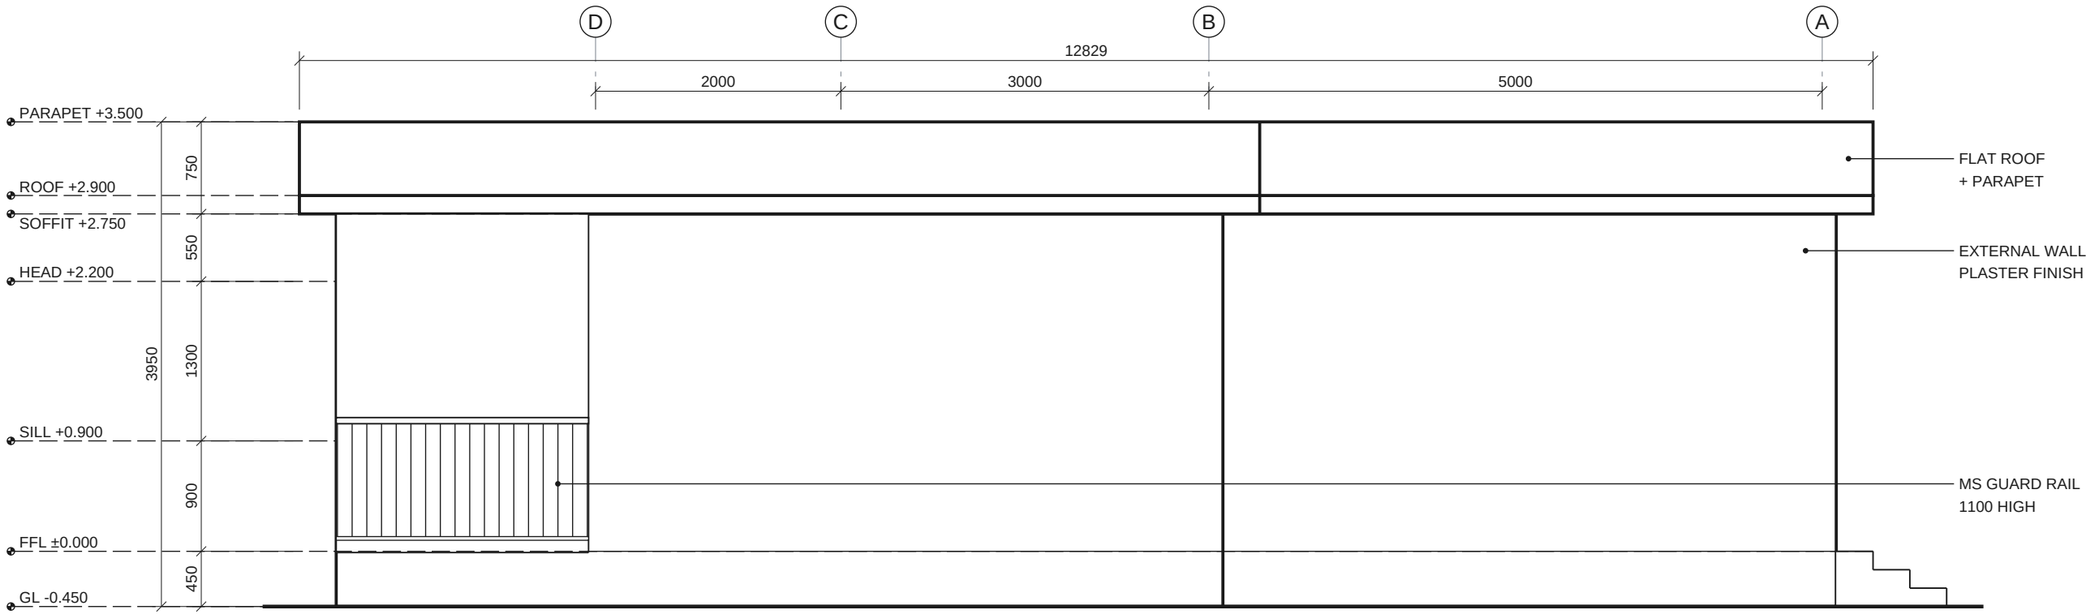

2 WEST ELEVATION

SCALE 1 : 50

GENERAL NOTES

1. ALL DIMENSIONS ARE IN MILLIMETRES; LEVELS ARE IN METRES FROM FFL ±0.000.
2. DO NOT SCALE FROM THIS DRAWING. USE FIGURED DIMENSIONS ONLY.
3. VERIFY ALL DIMENSIONS ON SITE BEFORE WORK AND REPORT ANY DISCREPANCY TO THE ARCHITECT.
4. READ WITH ALL SHEETS OF THIS SET. DOOR AND WINDOW MARKS AS THE SCHEDULE ON A-101.
5. WALLS 230 EXTERNAL / 115 INTERNAL BRICKWORK (HATCHED); COLUMNS, BEAMS, SLABS, LINTELS AND SILLS RCC (SOLID GREY).
6. BEAMS INDICATIVE: ROOF BEAMS 230 x 600 OVERALL INCL. SLAB; PLINTH BEAM 230 x 300. TO STRUCTURAL ENGINEER'S DESIGN.

PROJECT: STUDIO APARTMENT 101					1ST
DRAWING TITLE: EAST AND WEST ELEVATIONS			DRAWING NO.: A-202	STATUS: S2	REV: P01
DRAWN: SKETCH2MODEL	CHK'D: AUTOMATED	APPR'D: PENDING	DATE: 2026-10-18	SCALE: 1 : 50	SHEET: 3 / 4

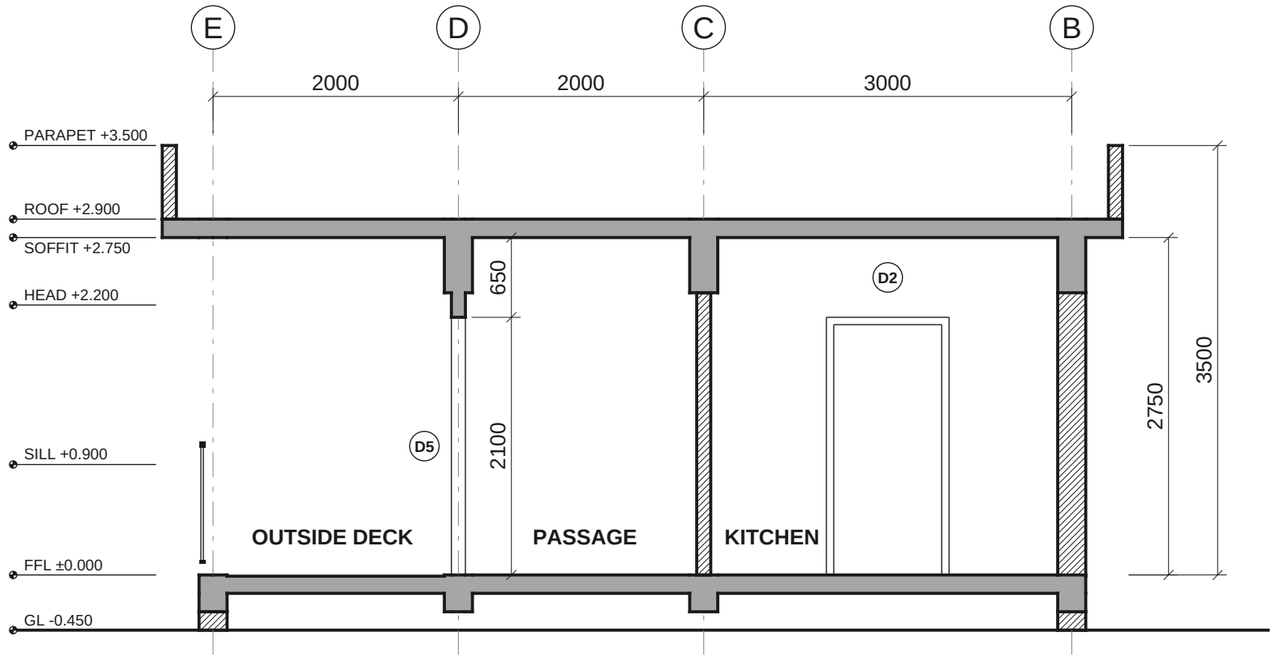

2 SECTION A-A

SCALE 1 : 50

GENERAL NOTES

1. ALL DIMENSIONS ARE IN MILLIMETRES; LEVELS ARE IN METRES FROM FFL ±0.000.
2. DO NOT SCALE FROM THIS DRAWING. USE FIGURED DIMENSIONS ONLY.
3. VERIFY ALL DIMENSIONS ON SITE BEFORE WORK AND REPORT ANY DISCREPANCY TO THE ARCHITECT.
4. READ WITH ALL SHEETS OF THIS SET. DOOR AND WINDOW MARKS AS THE SCHEDULE ON A-101.
5. WALLS 230 EXTERNAL / 115 INTERNAL BRICKWORK (HATCHED); COLUMNS, BEAMS, SLABS, LINTELS AND SILLS RCC (SOLID GREY).
6. BEAMS INDICATIVE: ROOF BEAMS 230 x 600 OVERALL INCL. SLAB; PLINTH BEAM 230 x 300. TO STRUCTURAL ENGINEER'S DESIGN.

PROJECT: STUDIO APARTMENT 101					1ST
DRAWING TITLE: SECTION A-A			DRAWING NO.: A-301	STATUS: S2	REV: P01
DRAWN: SKETCH2MODEL	CHK'D: AUTOMATED	APPR'D: PENDING	DATE: 2026-10-18	SCALE: 1 : 50	SHEET: 4 / 4