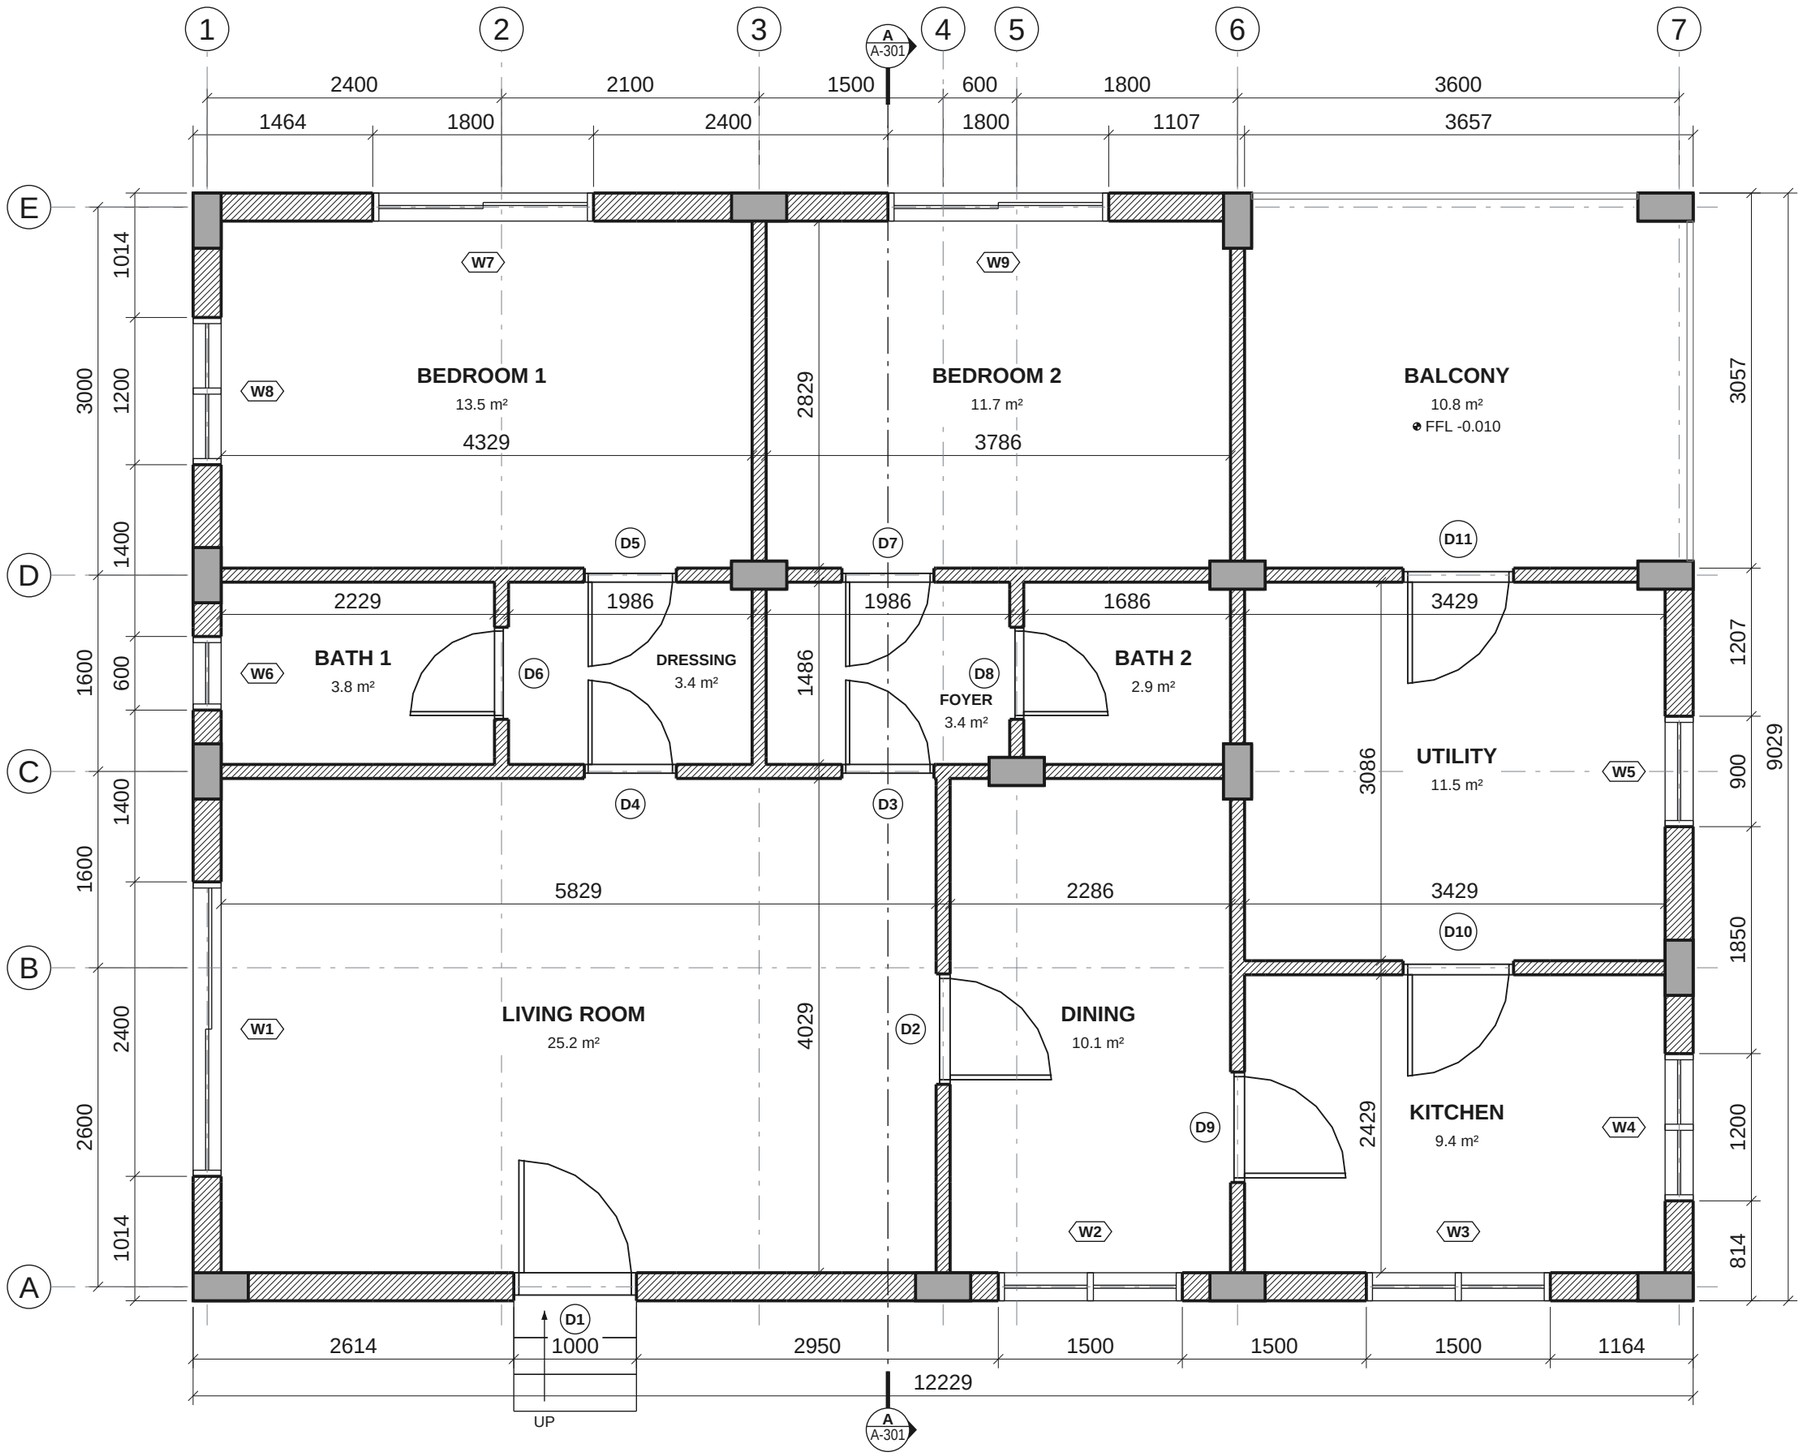


1 GROUND FLOOR PLAN

SCALE 1 : 50

DOOR & WINDOW SCHEDULE

MARK	W × H	SILL	HEAD	LOCATION
D1	1000 × 2100	—	2100	LIVING ROOM
D2	900 × 2100	—	2100	DINING
D3	750 × 2100	—	2100	FOYER
D4	750 × 2100	—	2100	DRESSING
D5	750 × 2100	—	2100	DRESSING
D6	750 × 2100	—	2100	BATH 1
D7	750 × 2100	—	2100	FOYER
D8	750 × 2100	—	2100	BATH 2
D9	900 × 2100	—	2100	KITCHEN
D10	900 × 2100	—	2100	KITCHEN
D11	900 × 2100	—	2100	UTILITY

MARK	W × H	SILL	HEAD	LOCATION
W1	2400 × 1300	900	2200	LIVING ROOM
W2	1500 × 1300	900	2200	DINING
W3	1500 × 1300	900	2200	KITCHEN
W4	1200 × 1300	900	2200	KITCHEN
W5	900 × 1300	900	2200	UTILITY
W6	600 × 1300	900	2200	BATH 1
W7	1800 × 1300	900	2200	BEDROOM 1
W8	1200 × 1300	900	2200	BEDROOM 1
W9	1800 × 1300	900	2200	BEDROOM 2


SIZES IN MM; SILL AND HEAD FROM FFL.

N

GENERAL NOTES


1. ALL DIMENSIONS ARE IN MILLIMETRES; LEVELS ARE IN METRES FROM FFL ±0.000.
2. DO NOT SCALE FROM THIS DRAWING. USE FIGURED DIMENSIONS ONLY.
3. VERIFY ALL DIMENSIONS ON SITE BEFORE WORK AND REPORT ANY DISCREPANCY TO THE ARCHITECT.
4. READ WITH ALL SHEETS OF THIS SET. DOOR AND WINDOW MARKS AS THE SCHEDULE ON A-101.
5. WALLS 230 EXTERNAL / 115 INTERNAL BRICKWORK (HATCHED); COLUMNS, BEAMS, SLABS, LINTELS AND SILLS RCC (SOLID GREY).
6. BEAMS INDICATIVE: ROOF BEAMS 230 WIDE x SPAN/10 DEEP; PLINTH BEAM 230 x 300. TO STRUCTURAL ENGINEER'S DESIGN.

PROJECT: SUNRISE RESIDENCY					1ST
DRAWING TITLE: GROUND FLOOR PLAN			DRAWING NO.: A-101	STATUS: S2	REV: P01
DRAWN: SKETCH2MODEL	CHK'D: AUTOMATED	APPR'D: PENDING	DATE: 2026-10-10	SCALE: 1 : 50	SHEET: 1 / 4

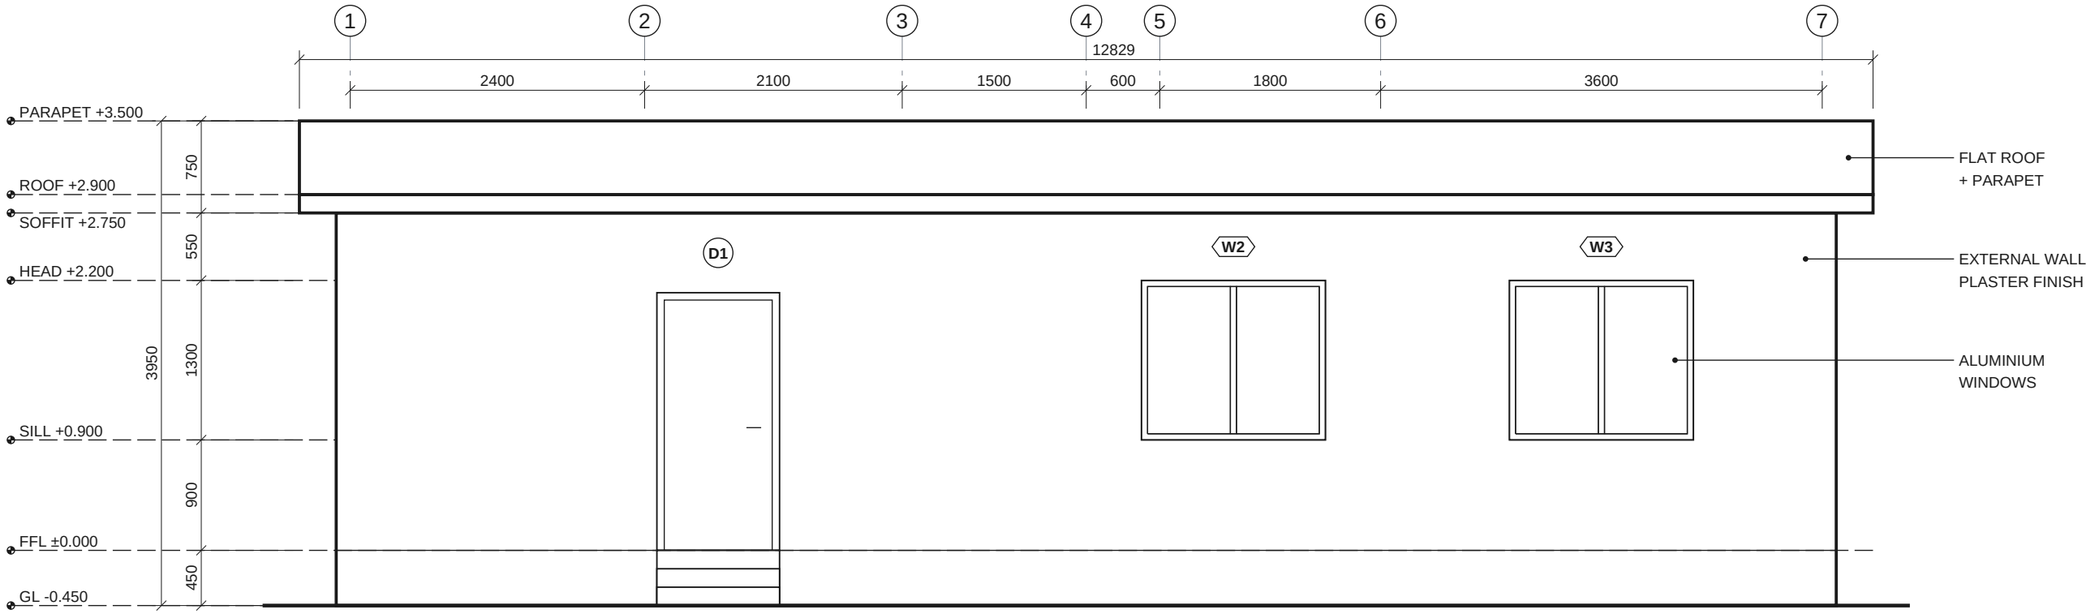

1 SOUTH ELEVATION

SCALE 1 : 50

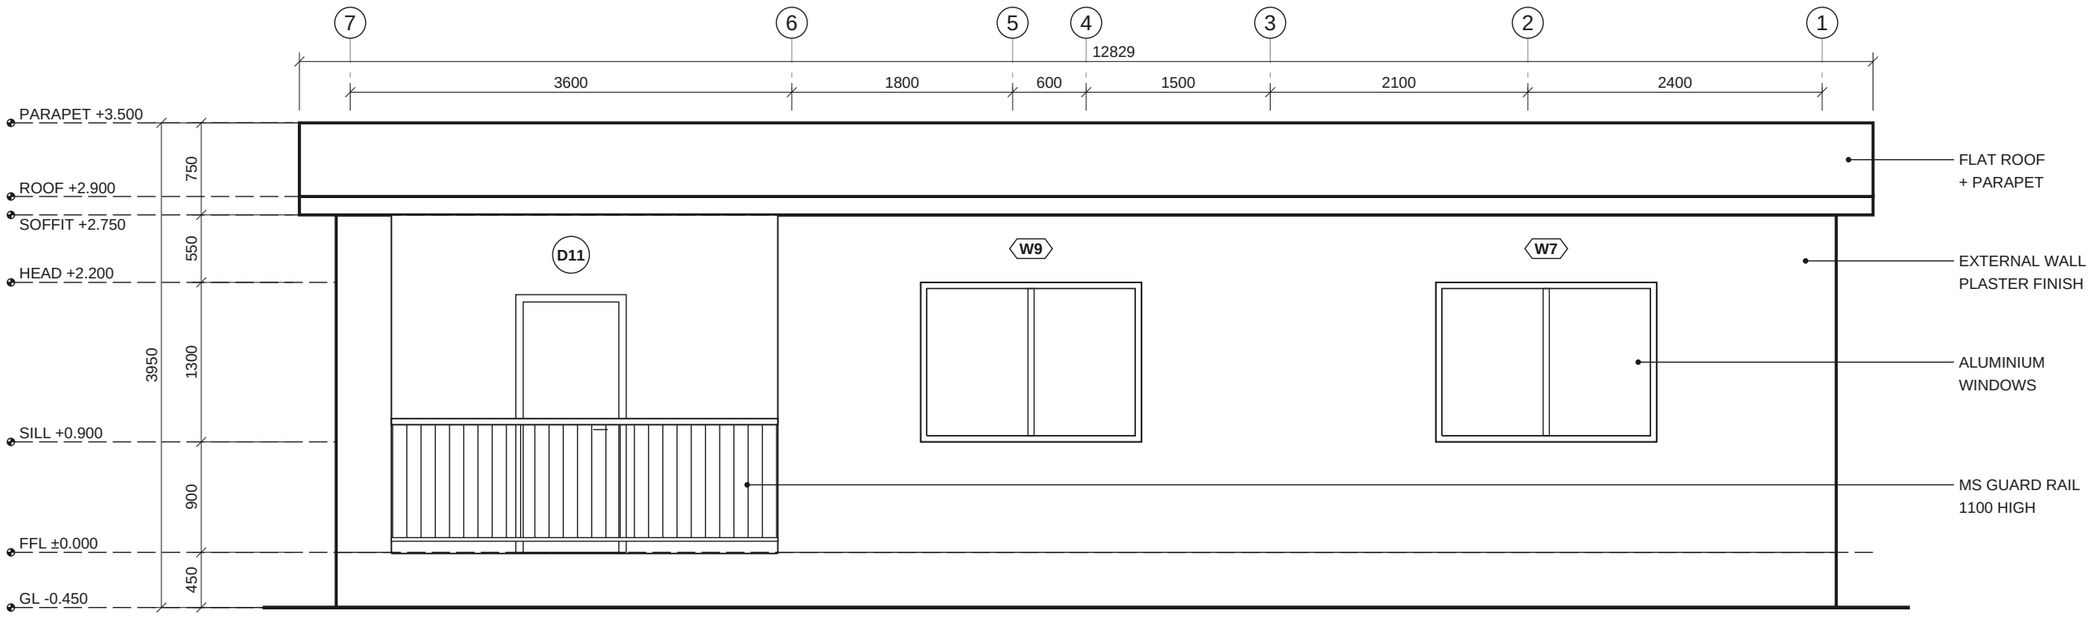


2 NORTH ELEVATION

SCALE 1 : 50

GENERAL NOTES


1. ALL DIMENSIONS ARE IN MILLIMETRES; LEVELS ARE IN METRES FROM FFL ±0.000.
2. DO NOT SCALE FROM THIS DRAWING. USE FIGURED DIMENSIONS ONLY.
3. VERIFY ALL DIMENSIONS ON SITE BEFORE WORK AND REPORT ANY DISCREPANCY TO THE ARCHITECT.
4. READ WITH ALL SHEETS OF THIS SET. DOOR AND WINDOW MARKS AS THE SCHEDULE ON A-101.
5. WALLS 230 EXTERNAL / 115 INTERNAL BRICKWORK (HATCHED); COLUMNS, BEAMS, SLABS, LINTELS AND SILLS RCC (SOLID GREY).
6. BEAMS INDICATIVE: ROOF BEAMS 230 WIDE x SPAN/10 DEEP; PLINTH BEAM 230 x 300. TO STRUCTURAL ENGINEER'S DESIGN.

PROJECT: SUNRISE RESIDENCY					1ST
DRAWING TITLE: SOUTH AND NORTH ELEVATIONS			DRAWING NO.: A-201	STATUS: S2	REV: P01
DRAWN: SKETCH2MODEL	CHK'D: AUTOMATED	APPR'D: PENDING	DATE: 2026-10-10	SCALE: 1 : 50	SHEET: 2 / 4

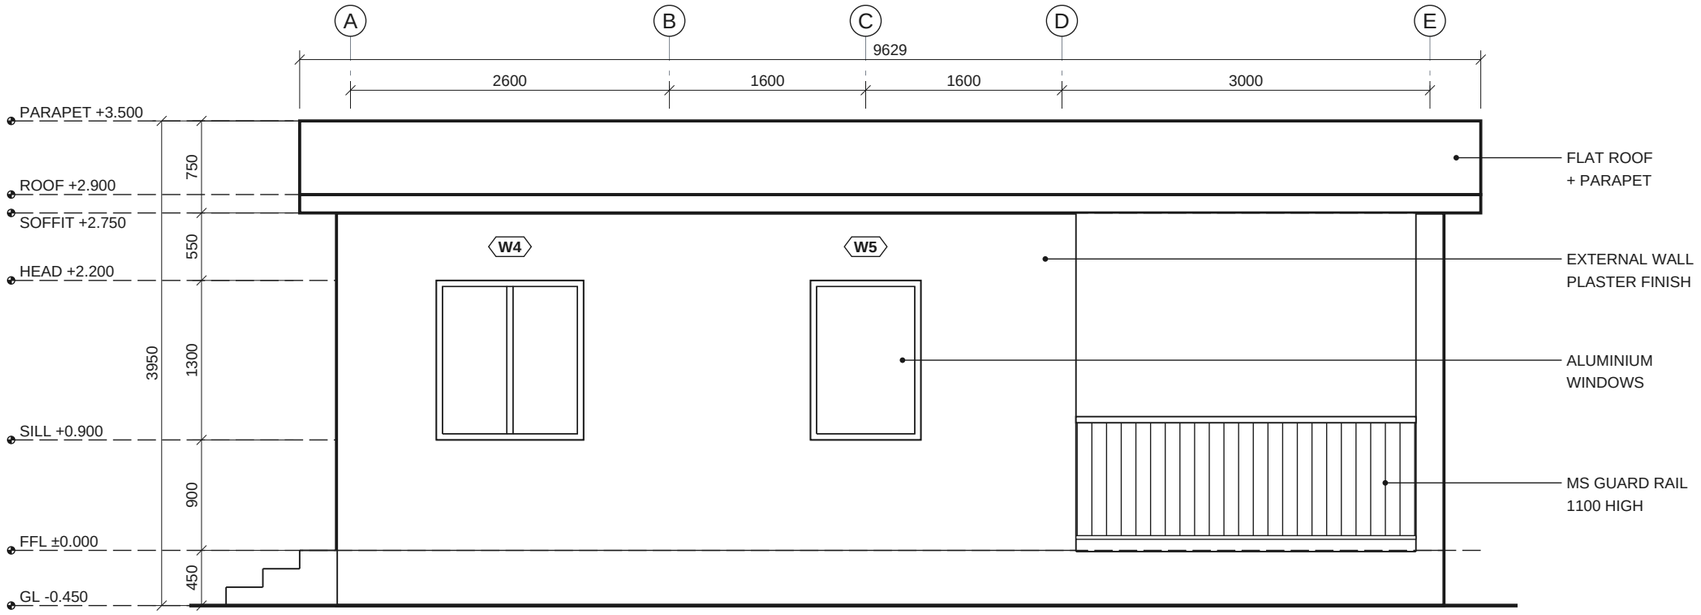

1 EAST ELEVATION

SCALE 1 : 50

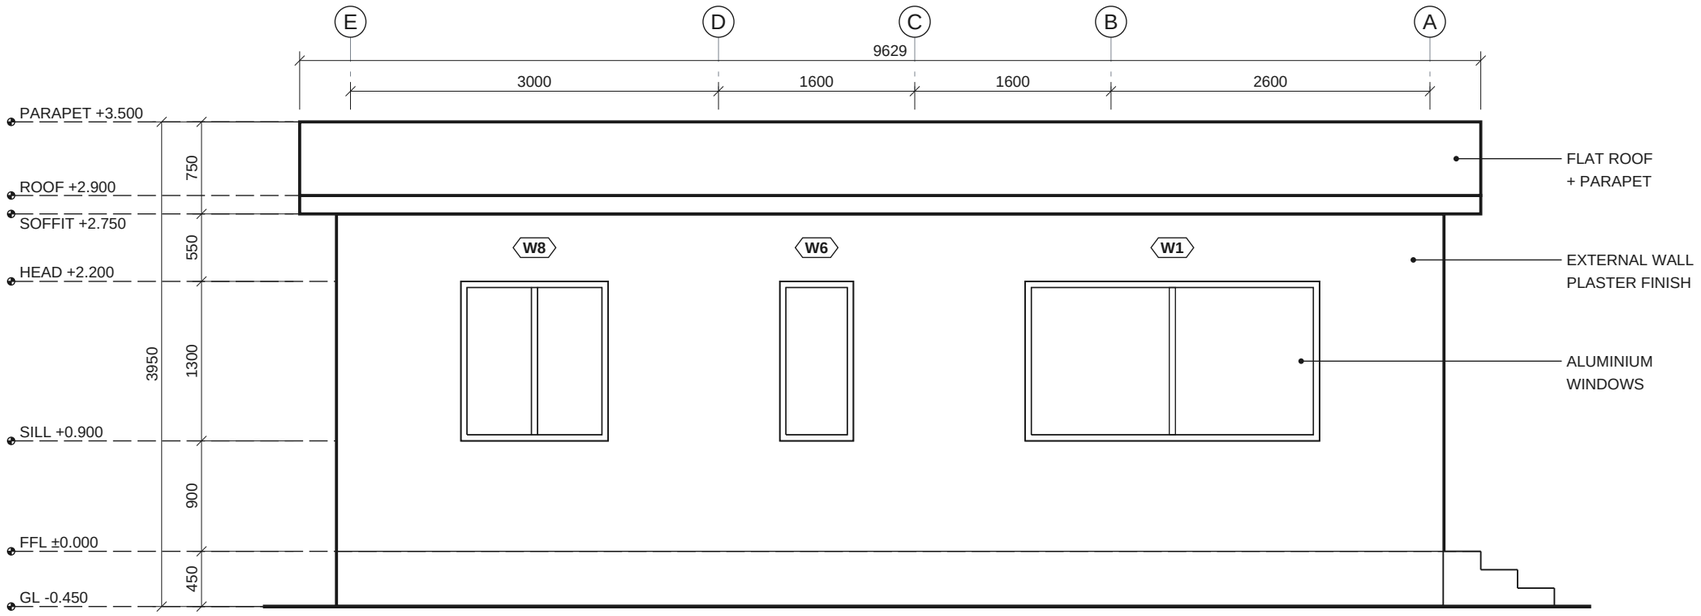


2 WEST ELEVATION

SCALE 1 : 50

GENERAL NOTES

1. ALL DIMENSIONS ARE IN MILLIMETRES; LEVELS ARE IN METRES FROM FFL ±0.000.
2. DO NOT SCALE FROM THIS DRAWING. USE FIGURED DIMENSIONS ONLY.
3. VERIFY ALL DIMENSIONS ON SITE BEFORE WORK AND REPORT ANY DISCREPANCY TO THE ARCHITECT.
4. READ WITH ALL SHEETS OF THIS SET. DOOR AND WINDOW MARKS AS THE SCHEDULE ON A-101.
5. WALLS 230 EXTERNAL / 115 INTERNAL BRICKWORK (HATCHED); COLUMNS, BEAMS, SLABS, LINTELS AND SILLS RCC (SOLID GREY).
6. BEAMS INDICATIVE: ROOF BEAMS 230 WIDE x SPAN/10 DEEP; PLINTH BEAM 230 x 300. TO STRUCTURAL ENGINEER'S DESIGN.

PROJECT: SUNRISE RESIDENCY					1ST
DRAWING TITLE: EAST AND WEST ELEVATIONS			DRAWING NO.: A-202	STATUS: S2	REV: P01
DRAWN: SKETCH2MODEL	CHK'D: AUTOMATED	APPR'D: PENDING	DATE: 2026-10-10	SCALE: 1 : 50	SHEET: 3 / 4

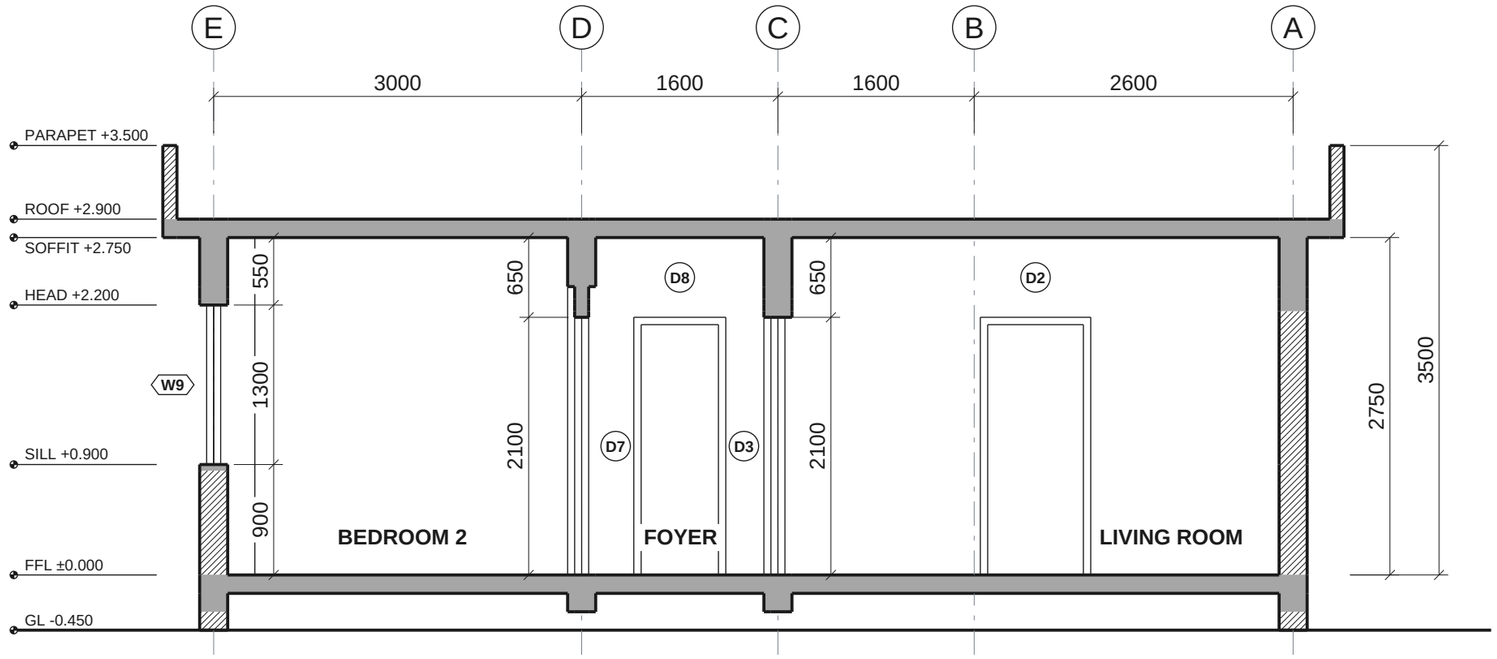

2 SECTION A-A

SCALE 1 : 50

GENERAL NOTES

1. ALL DIMENSIONS ARE IN MILLIMETRES; LEVELS ARE IN METRES FROM FFL ±0.000.
2. DO NOT SCALE FROM THIS DRAWING. USE FIGURED DIMENSIONS ONLY.
3. VERIFY ALL DIMENSIONS ON SITE BEFORE WORK AND REPORT ANY DISCREPANCY TO THE ARCHITECT.
4. READ WITH ALL SHEETS OF THIS SET. DOOR AND WINDOW MARKS AS THE SCHEDULE ON A-101.
5. WALLS 230 EXTERNAL / 115 INTERNAL BRICKWORK (HATCHED); COLUMNS, BEAMS, SLABS, LINTELS AND SILLS RCC (SOLID GREY).
6. BEAMS INDICATIVE: ROOF BEAMS 230 WIDE x SPAN/10 DEEP; PLINTH BEAM 230 x 300. TO STRUCTURAL ENGINEER'S DESIGN.

PROJECT: SUNRISE RESIDENCY					1ST
DRAWING TITLE: SECTION A-A			DRAWING NO.: A-301	STATUS: S2	REV: P01
DRAWN: SKETCH2MODEL	CHK'D: AUTOMATED	APPR'D: PENDING	DATE: 2026-10-10	SCALE: 1 : 50	SHEET: 4 / 4